
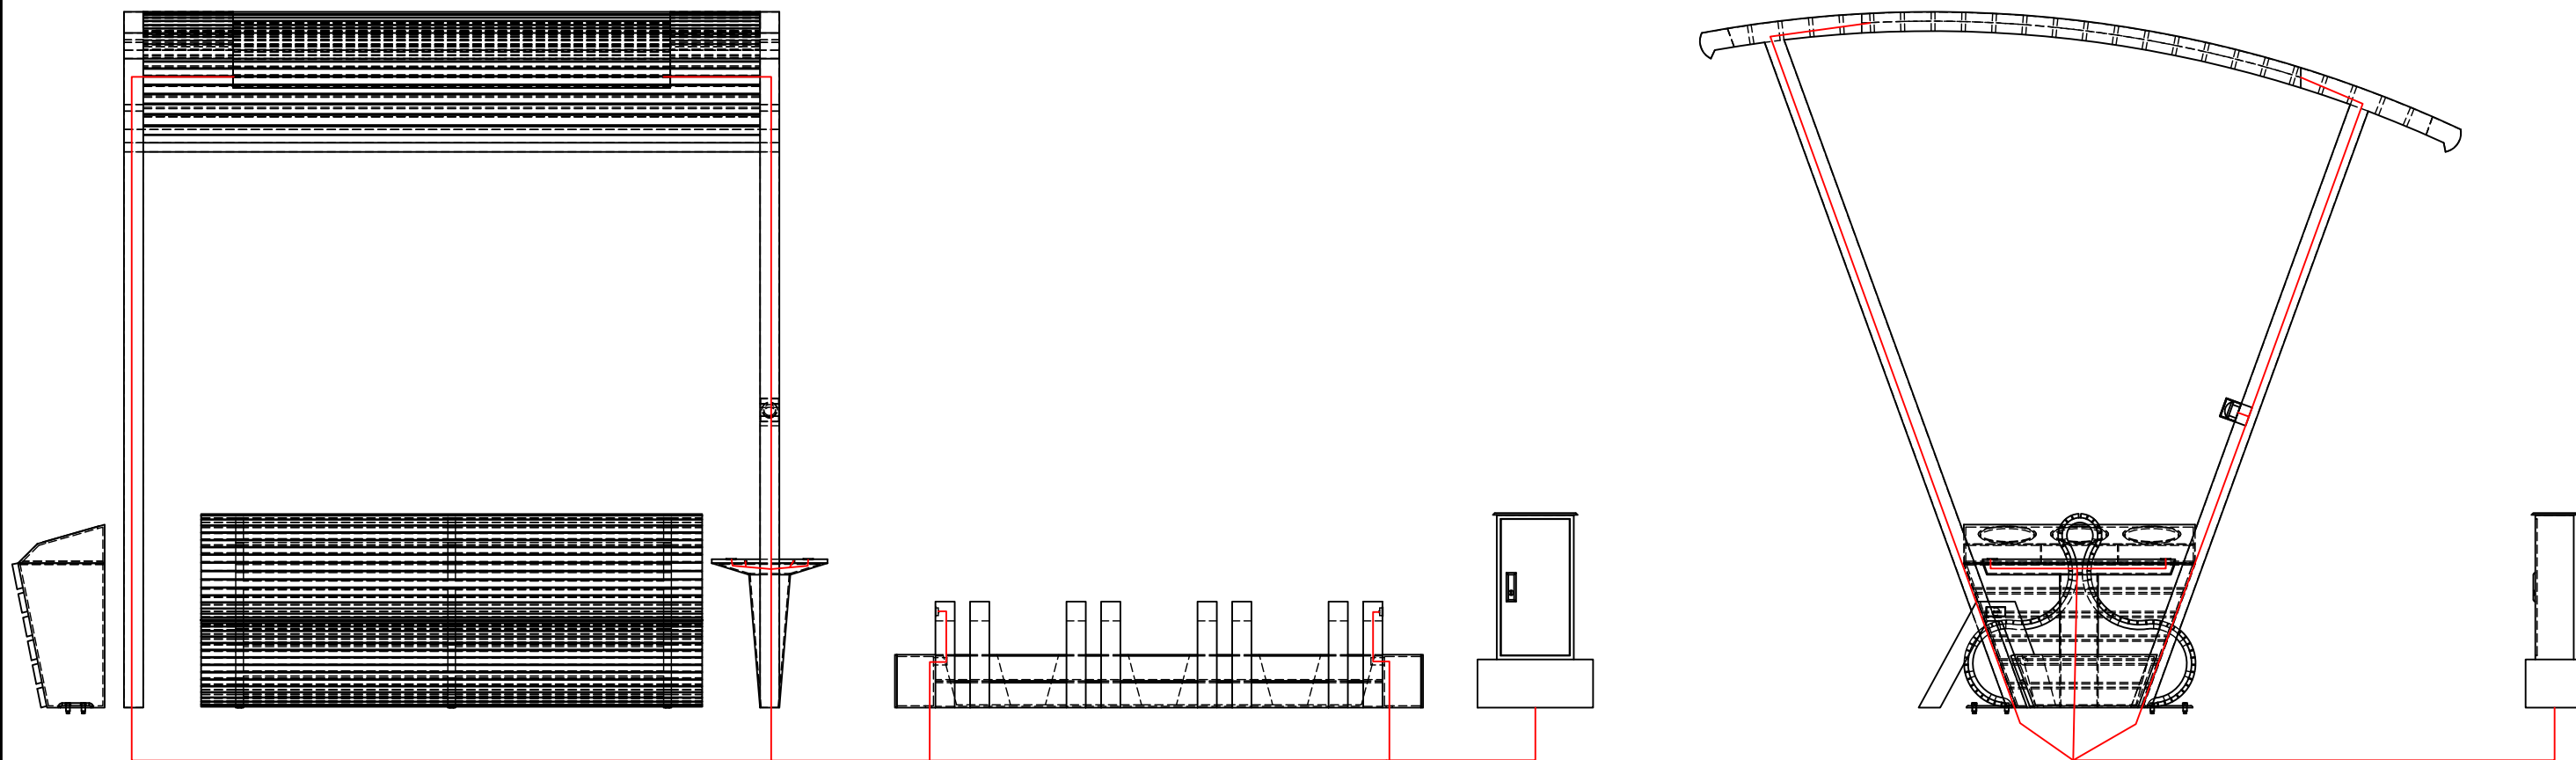


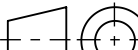

	APELLIDOS, NOMBRE	FECHA	Escuela de Ingenierías Industriales DISEÑO ASISTIDO POR ORDENADOR Curso 2025/26	
DIBUJADO	Biedma, Alejandro	09/05/26		
CORREGIDO				
Plano recorrido cableado			Lámina nº: 11	
			Material:	
			Escala: 1:35	
			Observaciones:	