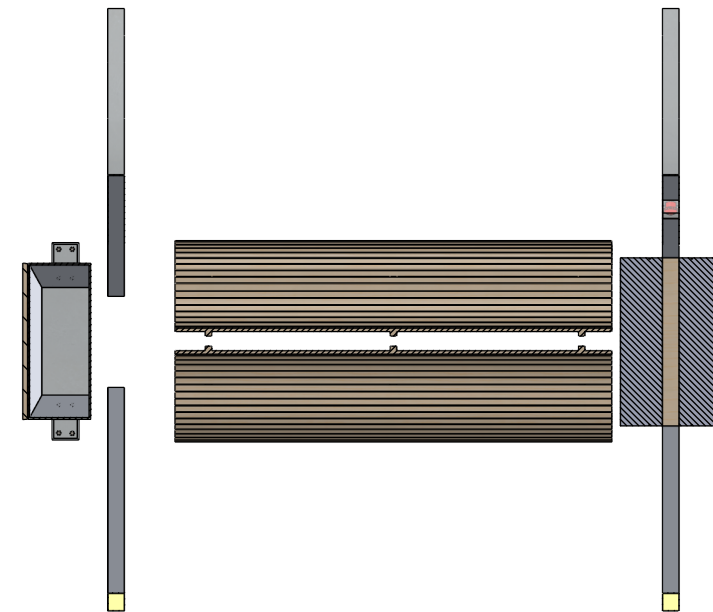
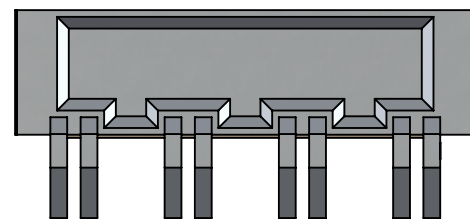
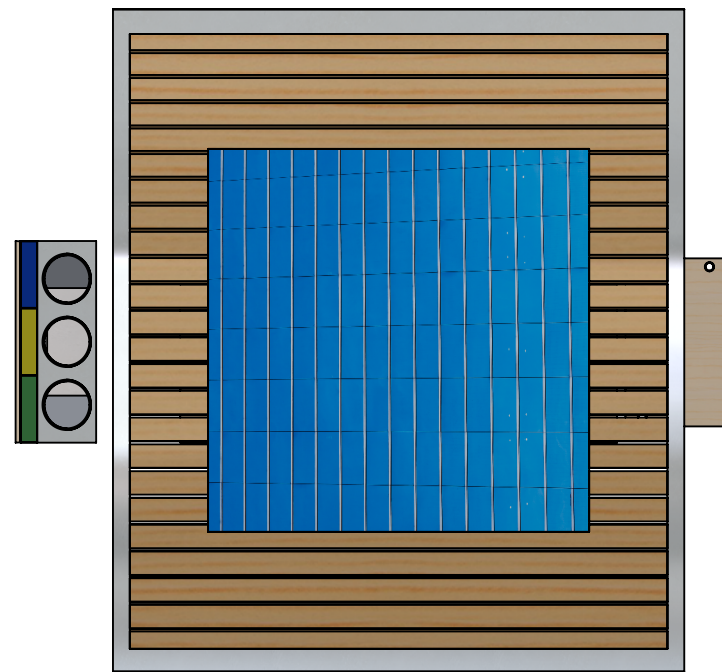
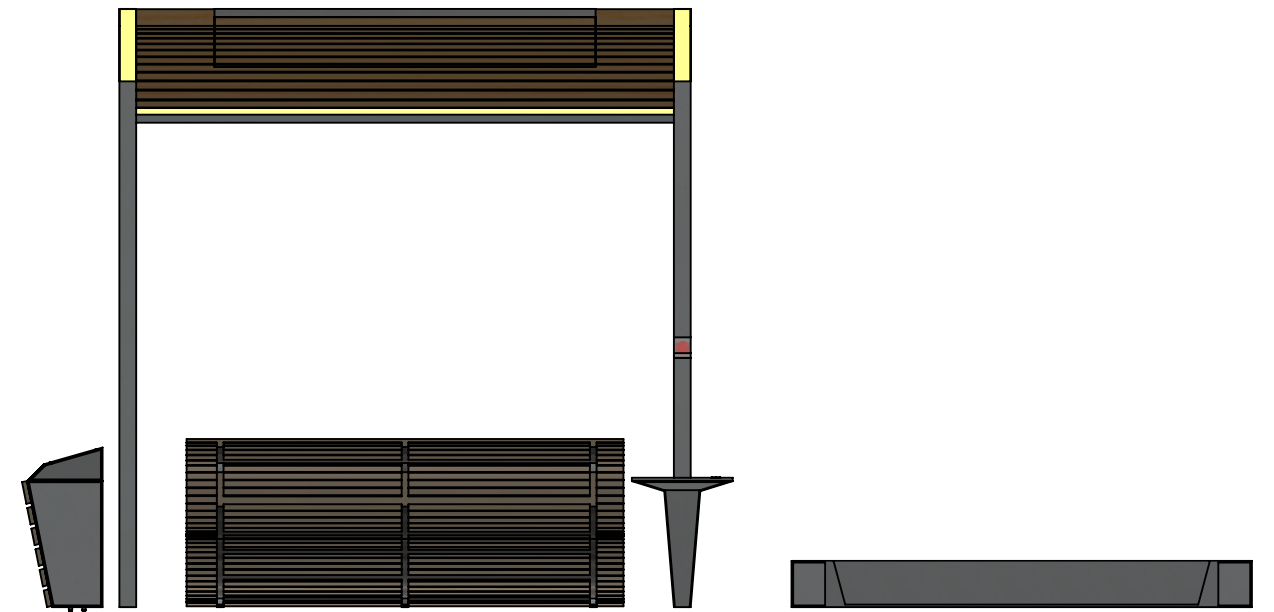
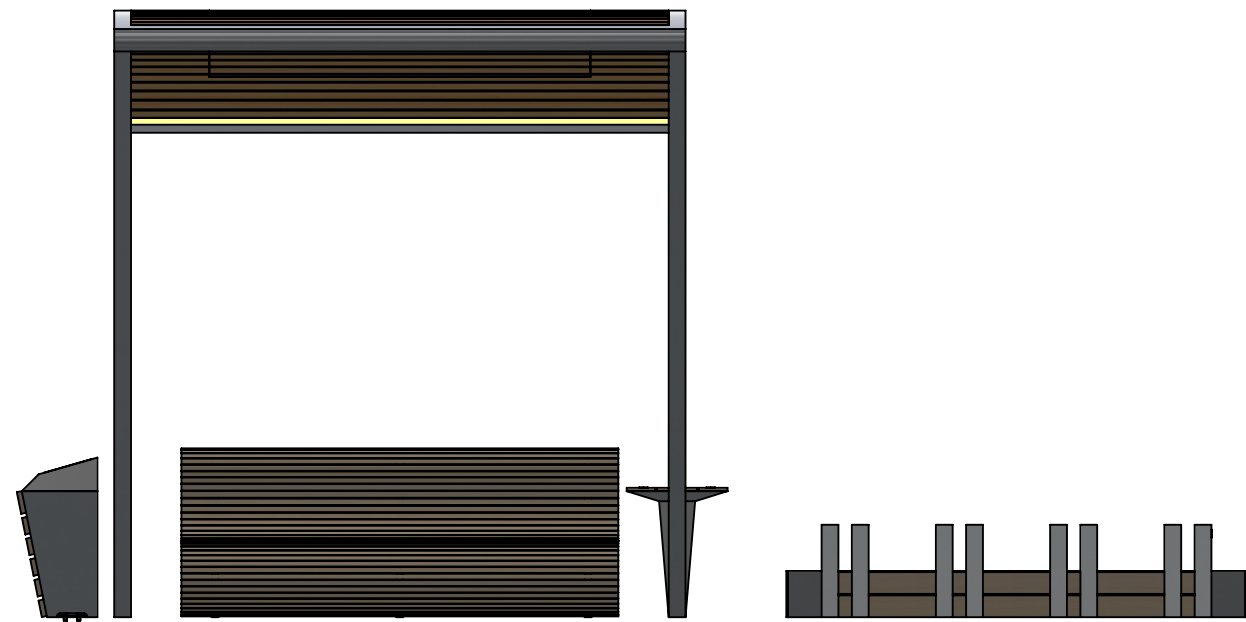
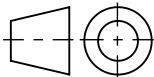


	APELLIDOS, NOMBRE	FECHA	Escuela de Ingenierías Industriales DISEÑO ASISTIDO POR ORDENADOR Curso 2025/26	
DIBUJADO	Biedma, Alejandro	09/05/26		
CORREGIDO				
Plano General 1			Lámina nº:2	
			Material:	
			Escala: 1:50	
			Observaciones:	