

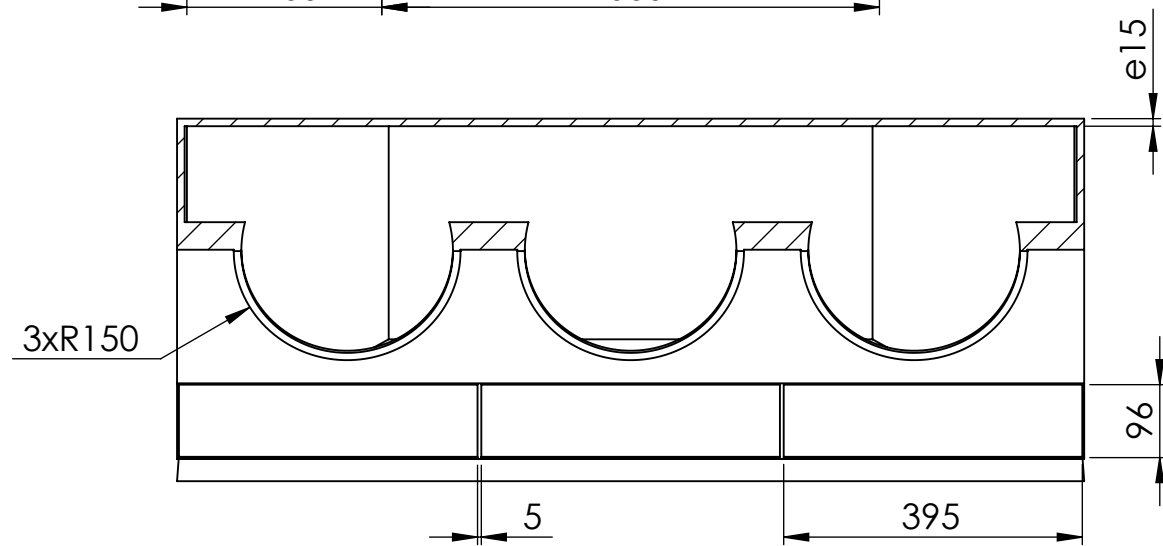
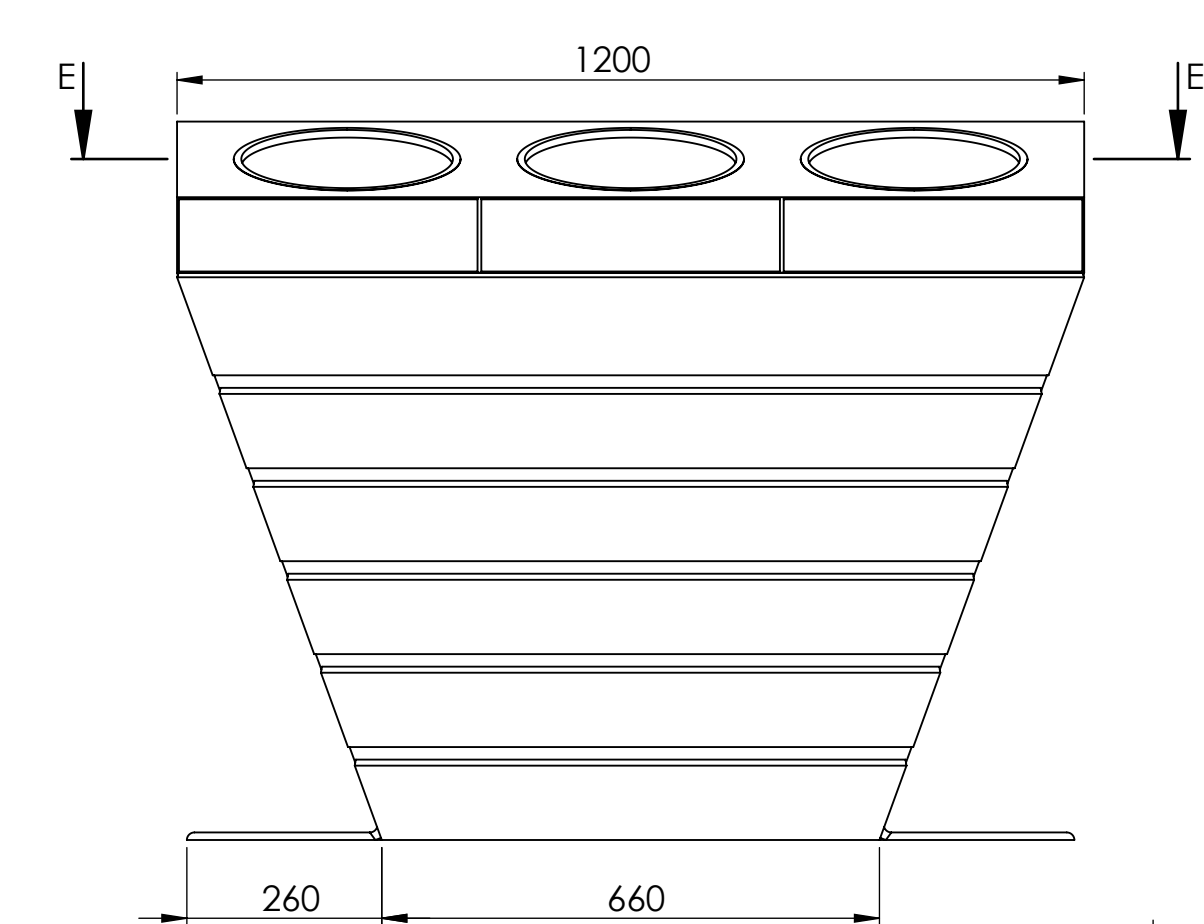
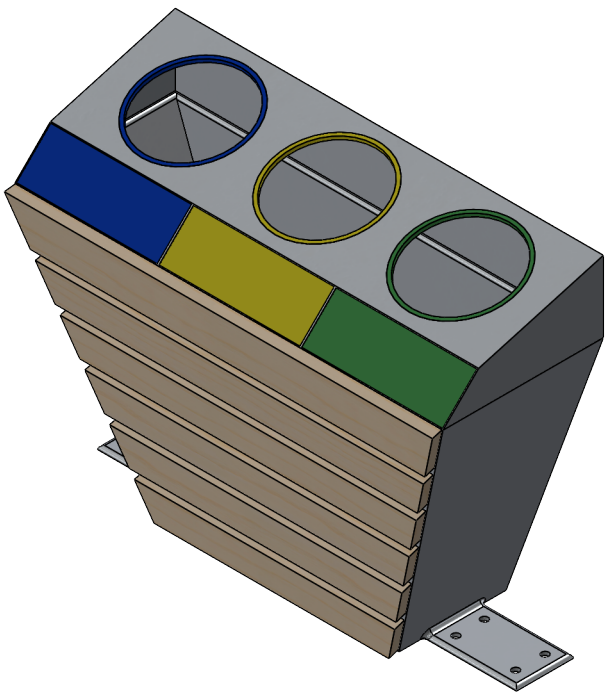
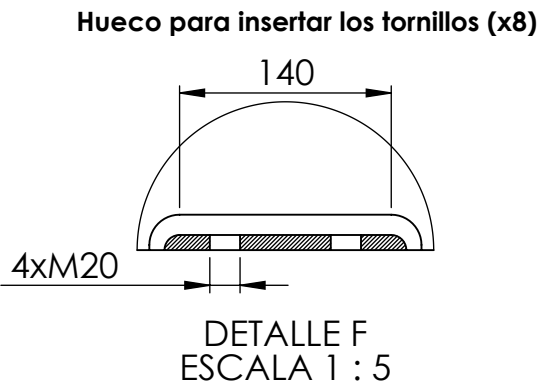
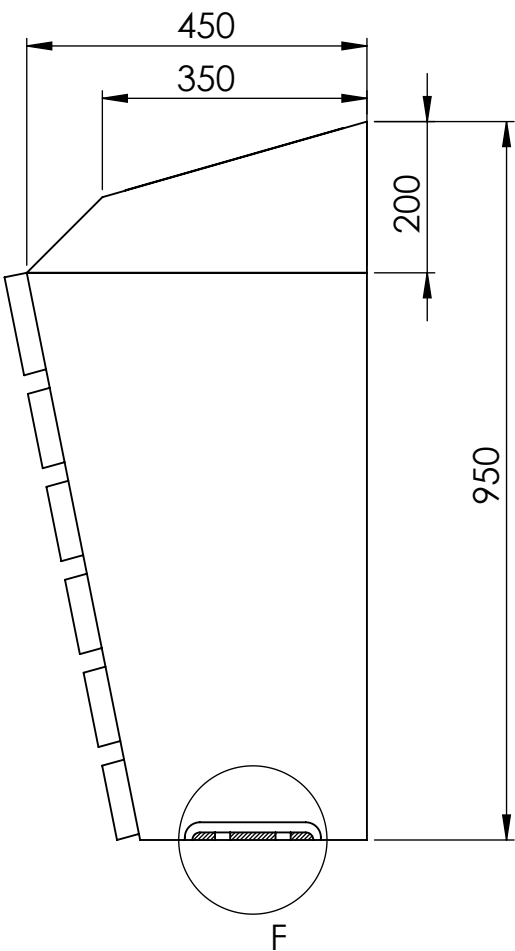


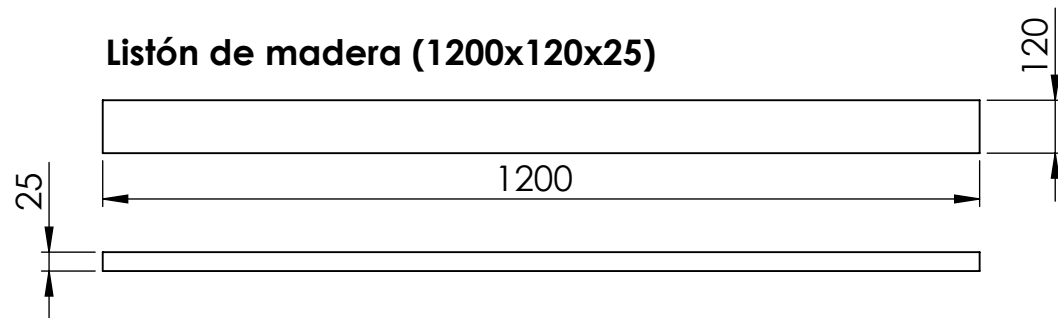

SECCIÓN E-E
ESCALA 1 : 10

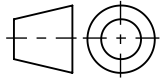

	APELLIDOS, NOMBRE	FECHA	Escuela de Ingenierías Industriales	
DIBUJADO	Biedma, Alejandro	09/05/26	DISEÑO ASISTIDO POR ORDENADOR	
CORREGIDO			Curso 2025/26	
Plano Papelera				Lámina nº: 6
				Material:
				Escala: 1 : 20
				Observaciones: