

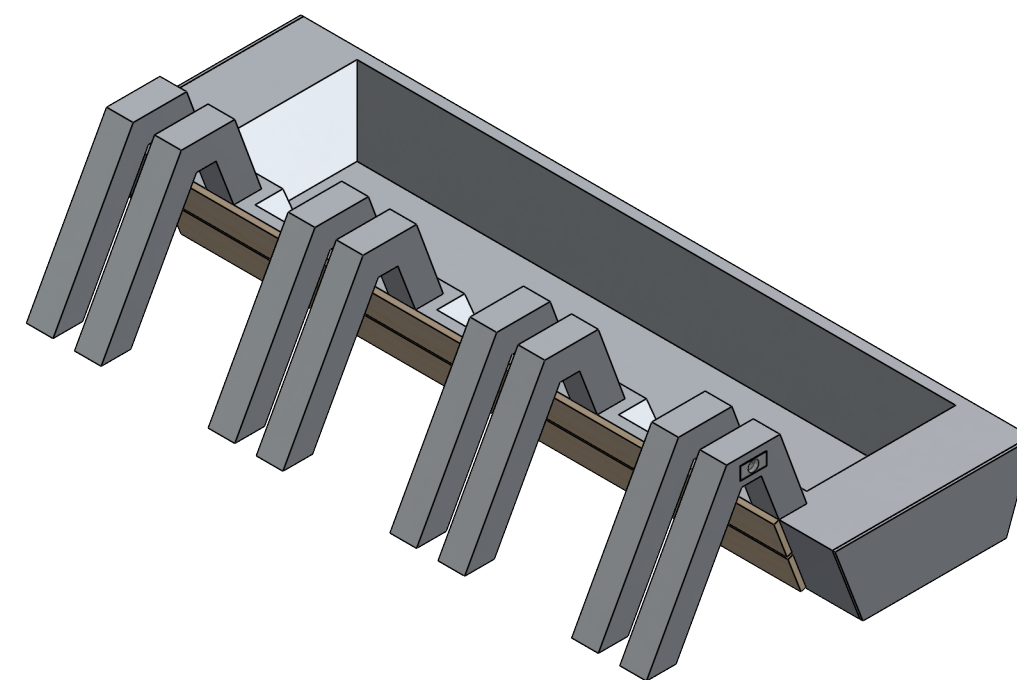
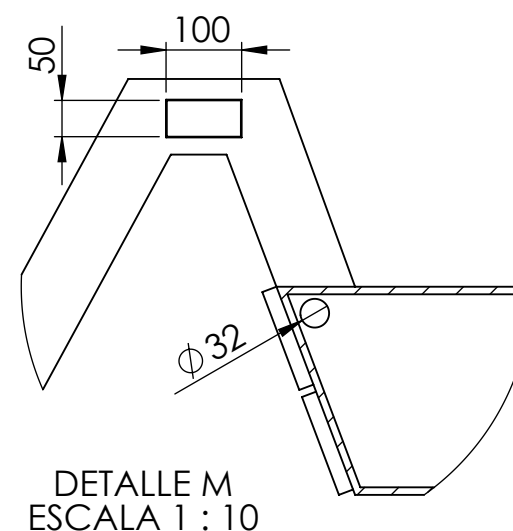
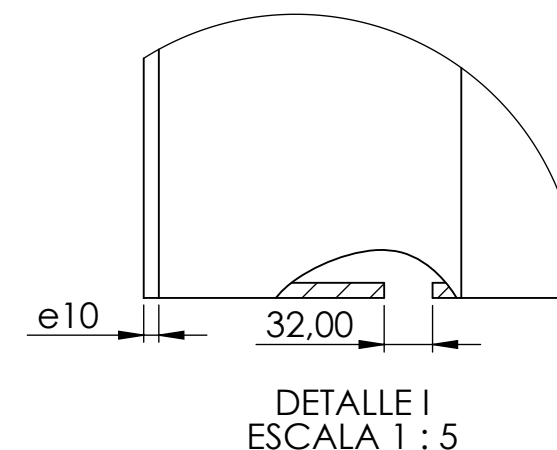
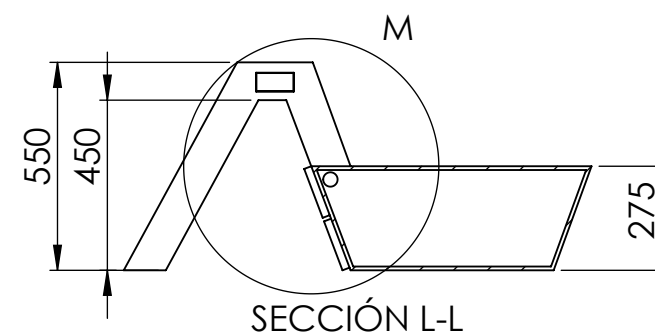


orificio para pasar cableado del enchufe
y zona de almacenamiento de la batería

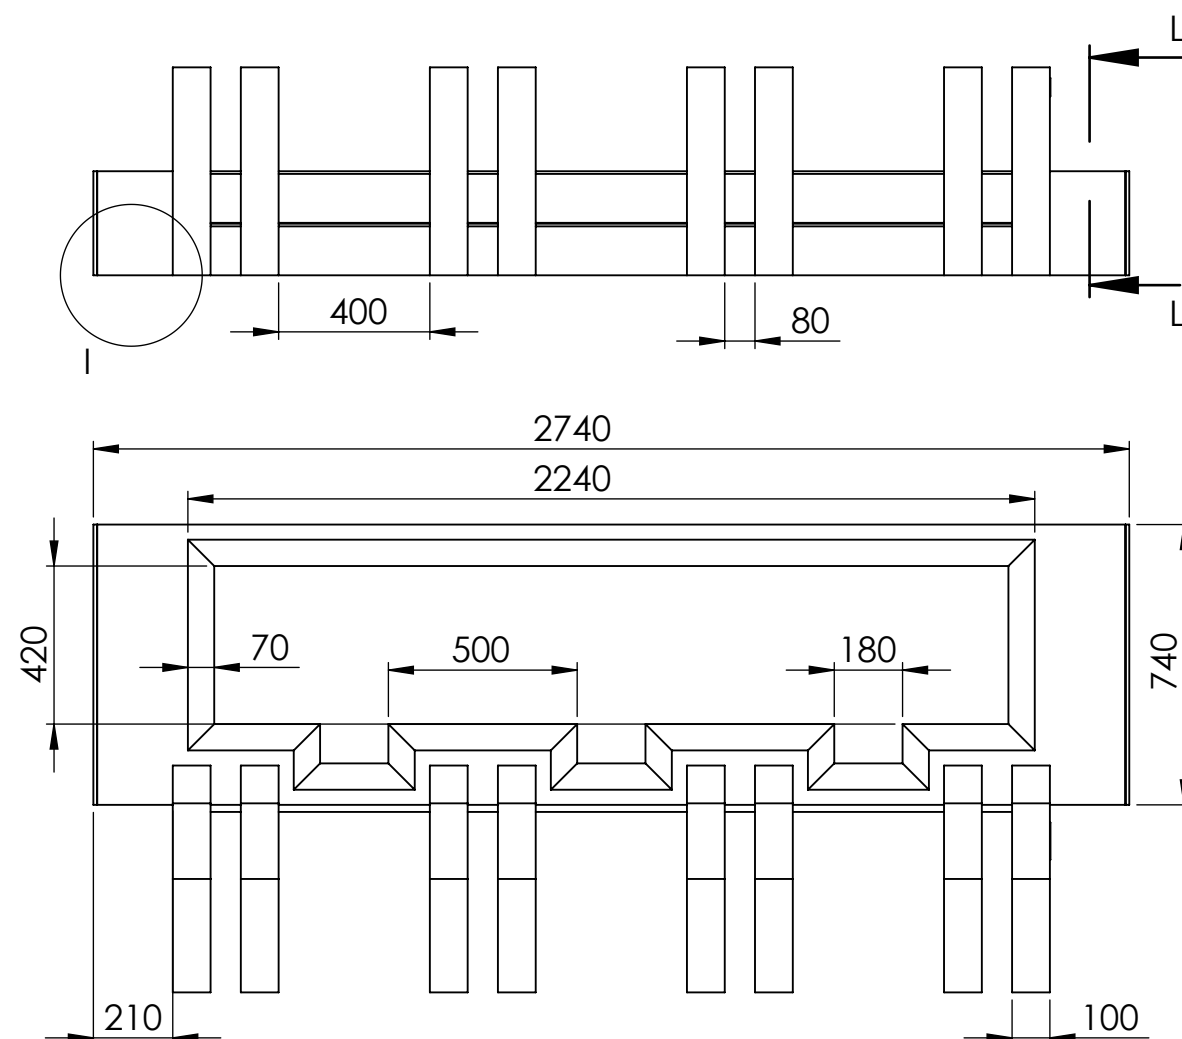

Listón de madera x2 (2320x140x40)

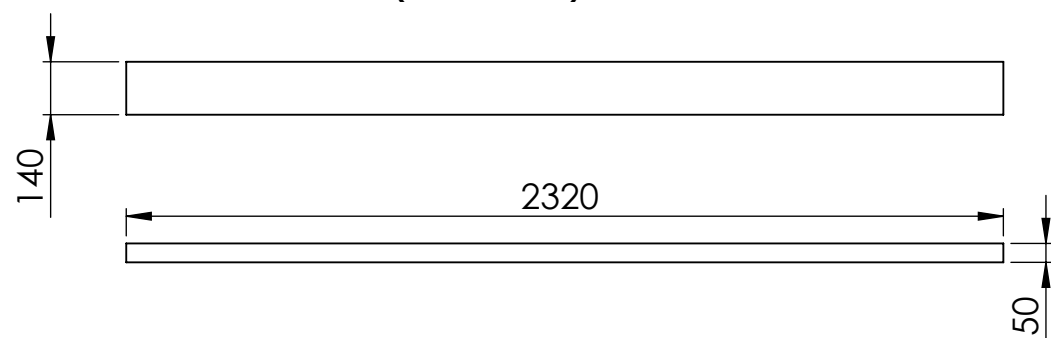

	APELLIDOS, NOMBRE	FECHA	Escuela de Ingenierías Industriales	
DIBUJADO	Biedma, Alejandro	09/05/26	DISEÑO ASISTIDO POR ORDENADOR	
CORREGIDO			Curso 2025/26	
Plano aparcabicis			Lámina n°: 8	
			Material:	
			Escala: 1:10	
			Observaciones:	